
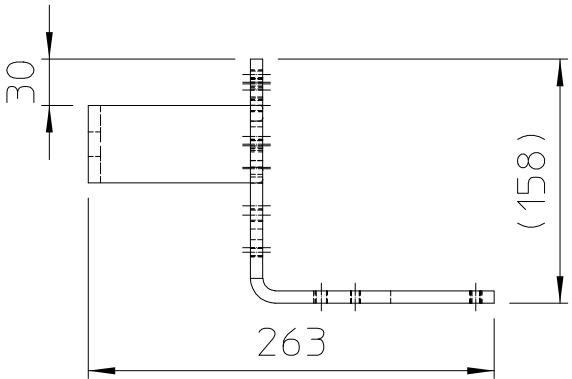
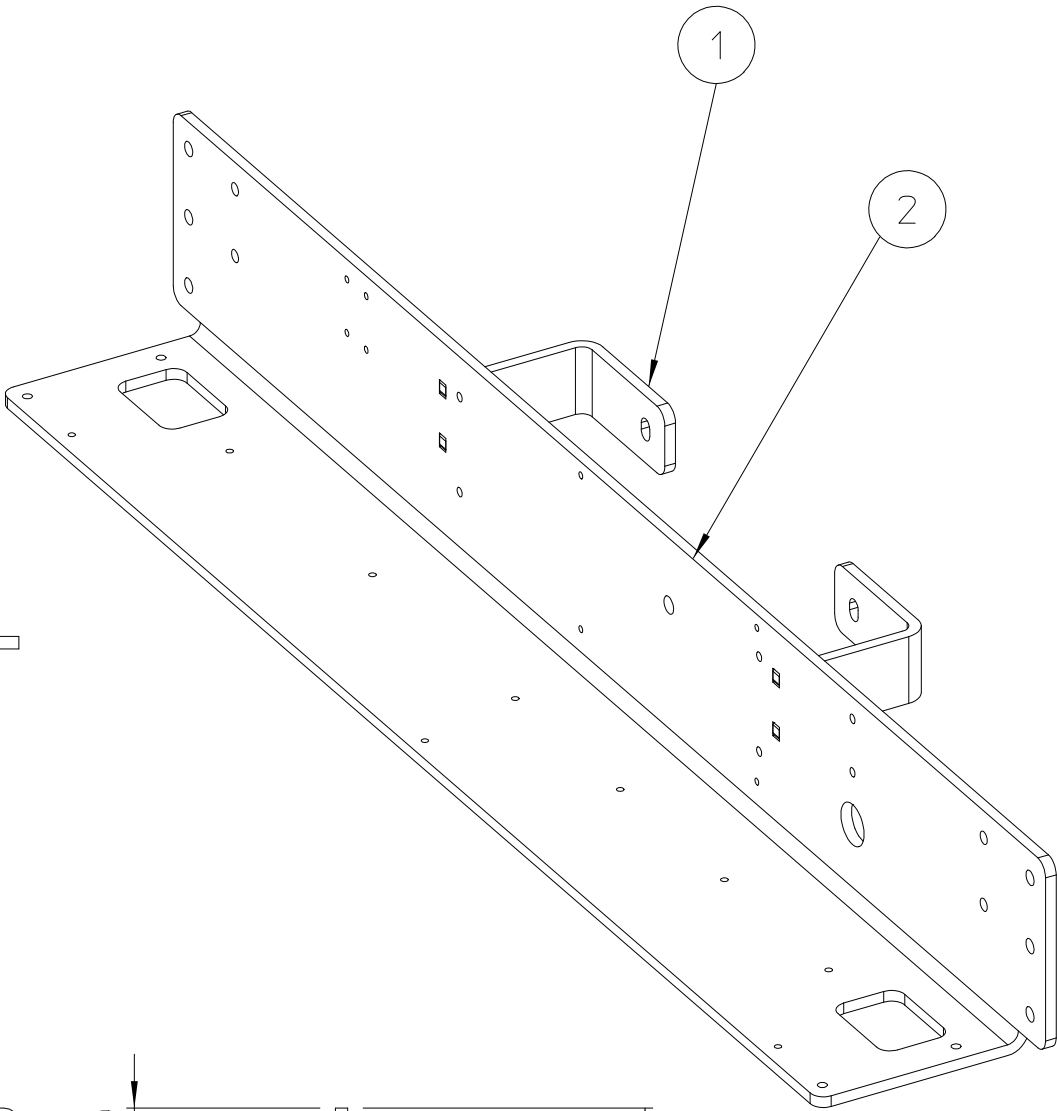
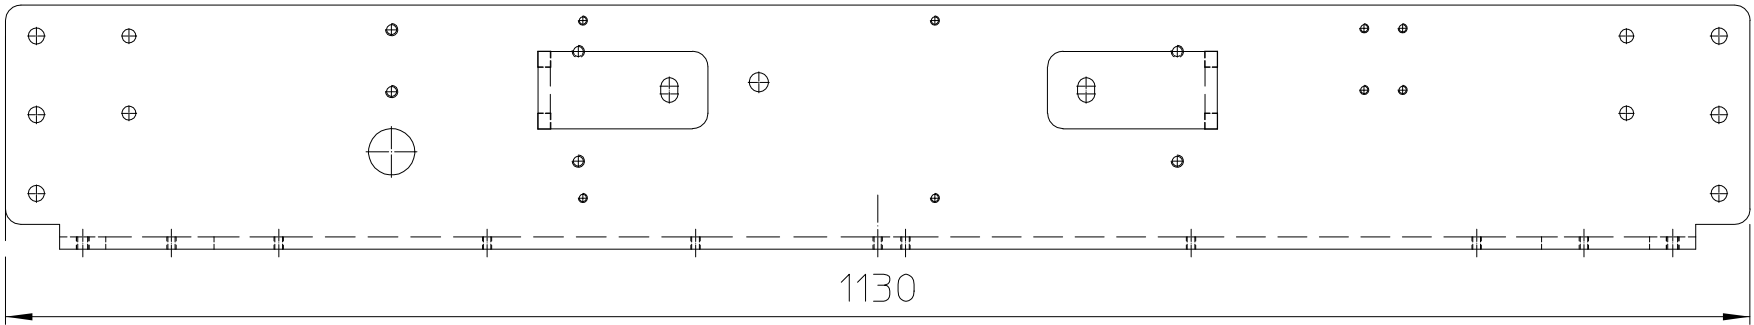


- General agreements for welded assemblies unless otherwise indicated:
- 1. Tube frames + end plates welded on all sides
 - 2. Sheet metal interrupted welding (weld 50 [mm], 100 [mm] free)
 - 3. Keep holes free of welds
 - 4. A height = thinnest sheet thickness / 2 + 1 = [mm]

Nok-verbindingen na lassen vlakslijpen
Coating Static

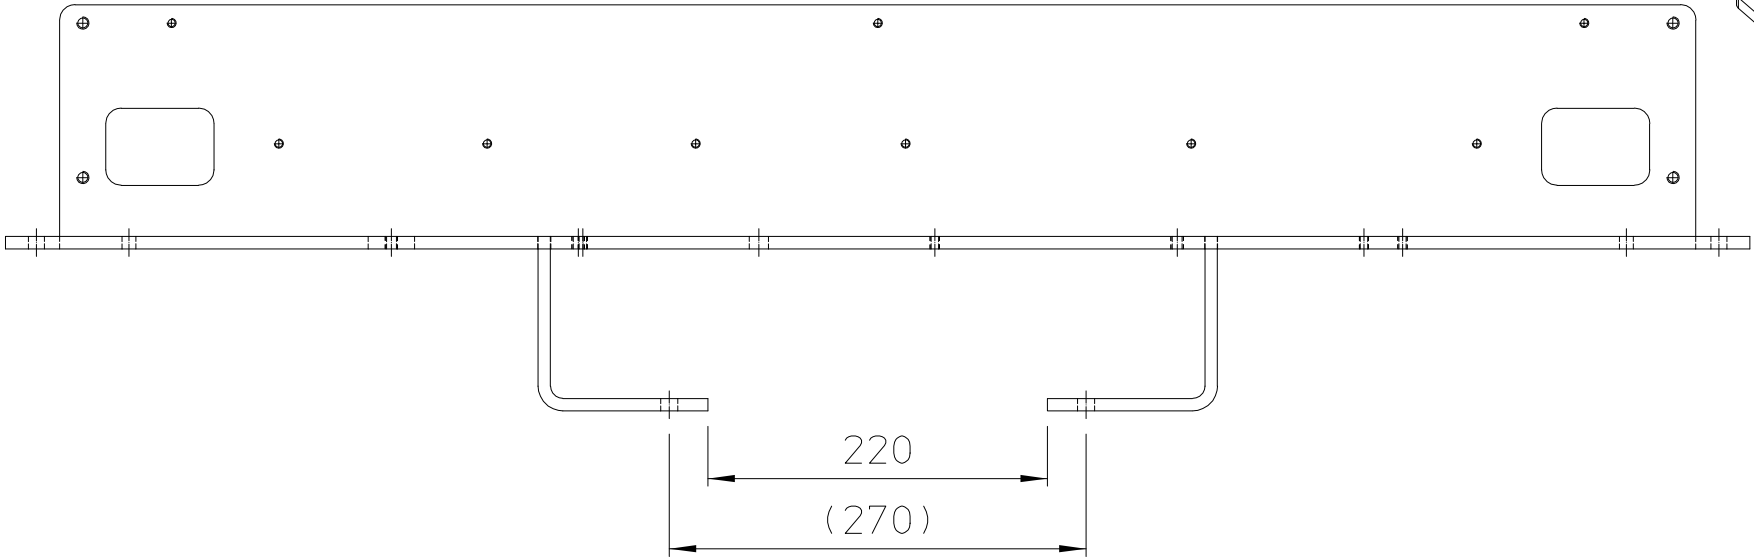

2	1	MD-22-07565	Frameplaat	St.37		
1	2	MD-19-04343	Bevestigingsplaat	St.37		
Pos. Nr	Aantal	Artikelnummer	Naam	Materiaal	Opmerking	
ruwheden volgens NEN 3632		plaats- en vormtol. volgens NEN 1101		toegestane afwijking niet getolereerde maten	0-20 20-200 200-2000 >2000	
scherpe kanten breken, seegerring-groeven scherp		maattoleranties volgens NEN 2731 Ⓔ		versp. bewerkingen	±0.2 ±0.5 ±1.0 ±2.0	
				plaat- en lasconstr.	±0.5 ±1.0 ±2.0 ±4.0	
titel: Sub-frame						
 logistic systems			get.:	RBE	ordernr.:	NIL
			datum:	27-Jan-25	klantnaam:	NIL
			gec.:	lk	mach.nr.:	NIL
			schaal:	1:5	bladnr./aantal:	
Deze tekening is eigendom van Elten Logistic Systems. Reproductie en inzage in enigerlei vorm aan derden is niet toegestaan. This drawing is property of Elten Logistic Systems. Reproduction or disclosure to a third party in any form is not allowed.			tekeningnummer:		revisie:	
			MD-22-07566		3	